

सौमित्र विहार योजना (नई जेल रोड भूमि विकास एवं गृहस्थान योजना) मोहनलालगंज लखनऊ

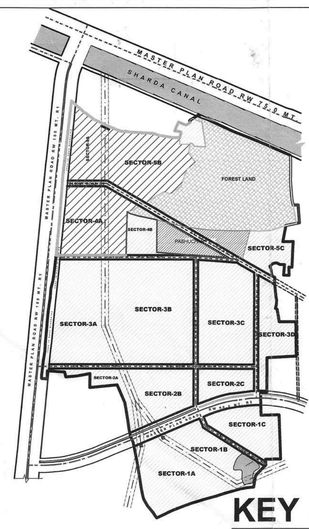

KEY PLAN

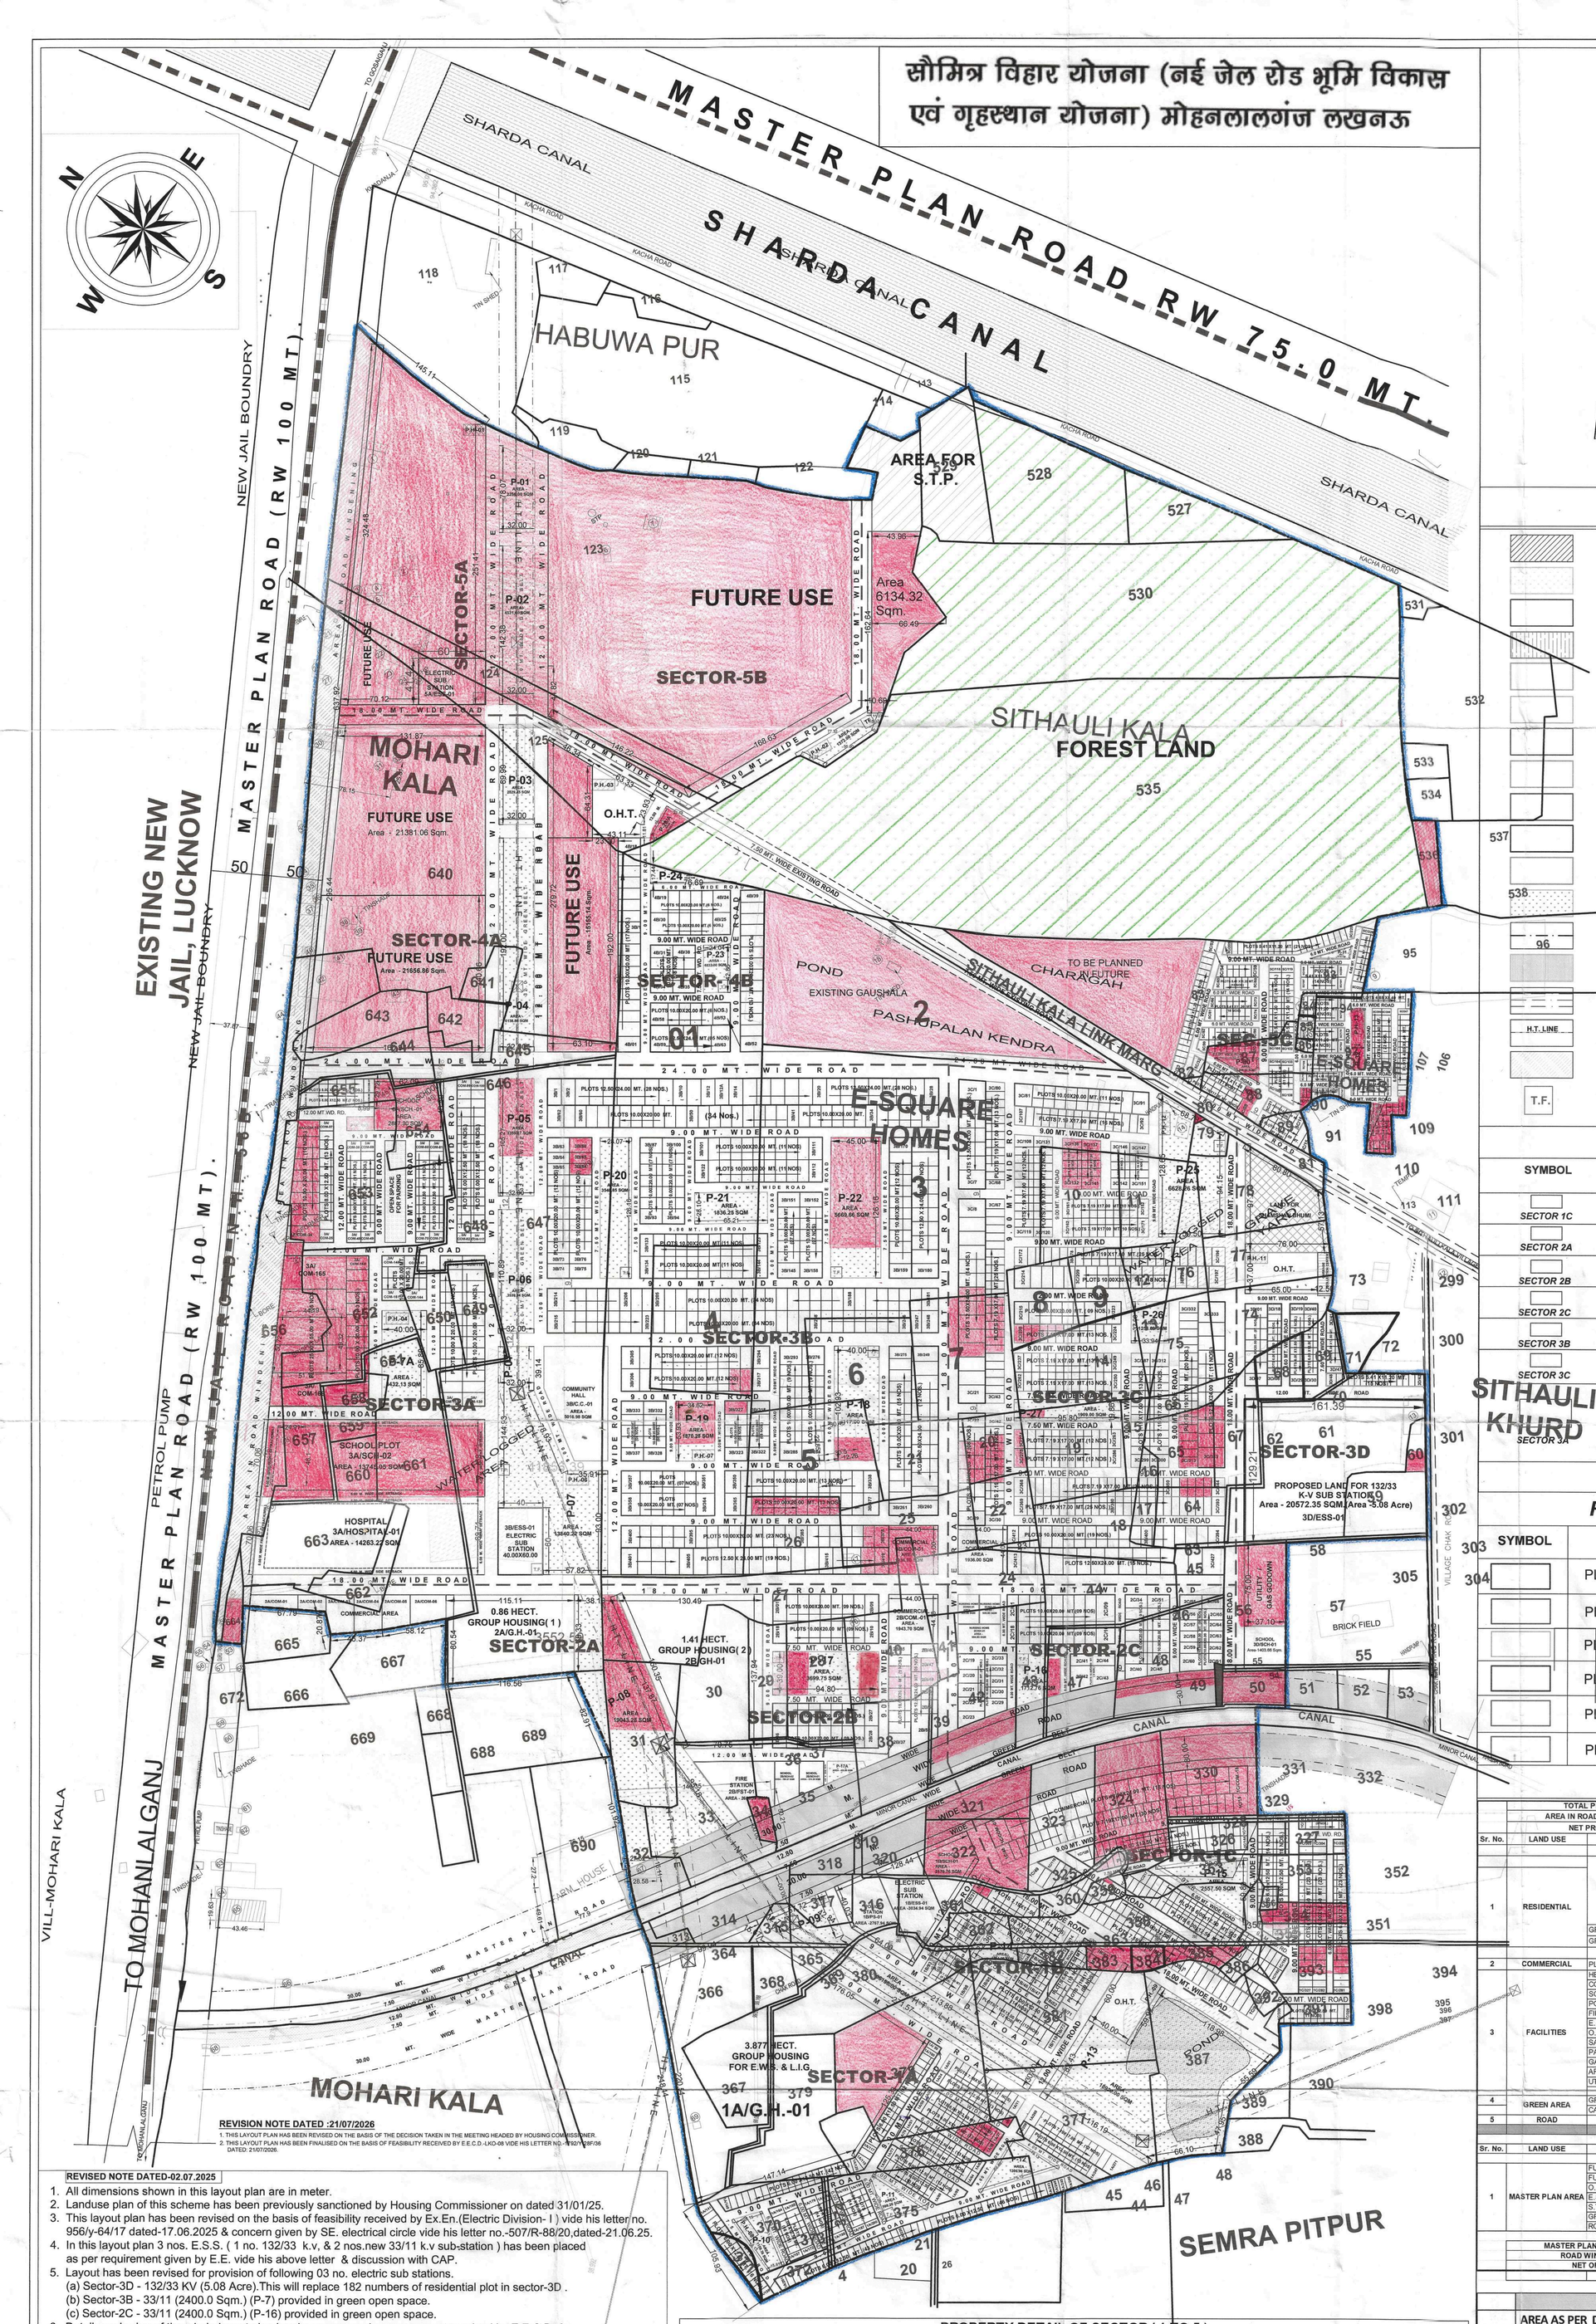

LEGEND

- MASTER PLAN USE
- FOREST LAND
- AREA LEFT FROM SCHEME FOR FUTURE USE
- GAUSHALA
- GROUP HOUSING
- HEALTH/NURSING HOME
- INSTITUTIONAL/SCHOOL
- GAS GODOWN
- FIRE/POLICE STATION/ PARISHAD SCHEME FACILITIES
- ELECTRIC SUB STATION 33/11
- COMMUNITY HALL
- GREEN
- SCHEME BOUNDARY
- CANAL
- ROAD
- H.T. LINE
- AREA IN ROAD WINDENING
- T.F. TRANSFORMER

LEGEND

- SCHEME BOUNDARY
- FOREST LAND
- AREA NOT TO BE REGISTERED IN RERA

JE AE EE

COMMERCIAL PLOT'S

SYMBOL	PLOT SIZE	AREA OF PLOT(SQM.)	NOS. OF PLOT
SECTOR 1C	PLOT-12.50 X 24.00 MT.	300	18
SECTOR 2A	-	4064.23	6
SECTOR 2B	PLOT-44.00 X 44.18 MT.	1943.70	1
SECTOR 2C	PLOT-44.00 X 44.18 MT.	1943.70	1
SECTOR 3B	PLOT-44.00 X 44.00 MT.	1936.00	1
SECTOR 3C	PLOT-44.00 X 44.00 MT.	1936.00	1
SECTOR 3A	PLOT-25.0 X 55.0 MT.	1375.00	5
	PLOT-10.00 X 20.0 MT.	200.00	57
	PLOT-8.00 X 12.50 MT.	100.00	107
	TOTAL		197

RESIDENTIAL PLOT'S

SYMBOL	PLOT SIZE	AREA OF PLOT (SQM.)	NOS. OF PLOT
	PLOT-12.5 X 24.0 MT.	300.00	140
	PLOT-10.0 X 20.0 MT.	200.00	570
	PLOT- 7.19 X 17.00 MT.	122.23	457
	PLOT- 6.00 X 12.50 MT.	75.00	614
	PLOT- 5.41 X 11.20 MT.	60.59	229
	PLOT- 4.85 X8.40 MT.	40.74	80
	TOTAL		2090

SECTOR	PLOT SIZE (SQM)	NO. OF PLOT	TOTAL (SQM)
3D	1403.66	01	1403.66
3C	1936.00	01	1936.00
3B	5016.98	01	5016.98
3A	200.00	34	6800.00
3A	100.00	107	10700.00
3A	14263.22	01	14263.22
2C	664.83	01	664.83
2C	505.85	02	1011.7
2B	780.97	01	780.97
2B	5744.59	01	5744.59
2B	2626.39	01	2626.39
2B	1943.70	01	1943.70
2B	14100.00	01	14100.00
2A	8600.00	01	8600.00
2A	4064.23/6	06	4064.23
1C	300.00	04	1200.00
1B	2767.94	01	2767.94
TOTAL	55784.13	165	78454.21

FOR RERA
124
548
375
540
207
77
1871

JE AE EE

	TOTAL PROJECT AREA		872710.00	SQM	
	AREA IN ROAD WINDENING AREA		12743.70	SQM	
	NET PROJECT AREA		859966.30	SQM	
Sr. No.	LAND USE	SUB-LAND USE	TYPE	NOS.	AREA IN SQM	%
				approx		
1	RESIDENTIAL	PLOTTED DEVLOPMENT	12.50 X 24.00	140	41856.39	4.87%
			10.0 X 20.0	570	122740.7	14.27%
			7.19 X 17.00	457	59294.72	6.90%
			6.00x 12.50	614	49221.34	5.72%
			5.41 x 11.20	229	15301.36	1.78%
			4.85 x 8.40	80	3552.59	0.41%
		GROUP HOUSING		2	22758.12	2.65%
		GROUP HOUSING(EWS/LIG)		1	38779.56	4.51%
					353504.78	41.11% 41.11%
2	COMMERCIAL	PLOTS		197	47646.48	5.54% 5.54%
3	FACILITIES	HEALTH/NURSNG HOME		4	15421.6	1.79%
		COMMUNITY		1	5016.98	0.58%
		SCHOOLS		6	22089.52	2.57%
		POLICE		1	2771.79	0.32%
		FIRE STATION		1	2826.39	0.31%
		E.S.S.		4	28491.54	3.31%
		O.H.T.		3	4805.00	0.56%
		SAMSHAN BHOMI		1	5540.25	0.64%
		PARKING AREA		2	2001.16	0.23%
		GARBAGE/COLLECTION CENTER		1	474.50	0.06%
		AREA FOR S.T.P.		1	10998.19	1.28%
		UTILITY (GAS GODOWN)		1	2782.07	0.32%
					1034 8.33	11.86% 11.86%
4	GREEN AREA	GREEN/TRANSFORMER/P.H.			1145.19.63	13.36% 13.76%
		CANAL			3395.94	0.40%
5	ROAD				237486.48	27.62% 27.62%
		TOTAL			859966.30	100.00%

Sr. No.	LAND USE	SUB-LAND USE	TYPE	NOS.	AREA IN SQM	%
1	MASTER PLAN AREA	FUTURE USE		0	110816.21	50.92%
		FUTURE USE		0	42403.53	19.48%
		O.H.T.		1	2354.43	1.08%
		E.S.S.		1	2484.24	1.14%
		S.T.P.		1	4313.84	1.98%
		GREEN			15785.92	7.24%
		ROAD			39507.08	18.15%
		TOTAL			217645.25	100.00%

MASTER PLAN OFFICE USE AREA	230828.00	SQM
ROAD WINDENING AREA	13182.75	SQM
NET OFFICE AREA	217645.25	SQM

REVISION NOTE DATED :21/07/2026

1. THIS LAYOUT PLAN HAS BEEN REVISED ON THE BASIS OF THE DECISION TAKEN IN THE MEETING HEADED BY HOUSING COMMISSIONER.
2. THIS LAYOUT PLAN HAS BEEN FINALISED ON THE BASIS OF FEASIBILITY RECEIVED BY E.E.C.D.-LKO-08 VIDE HIS LETTER NO.-4792/Y-SR/26 DATED: 21/07/2026.

REVISED NOTE DATED-02.07.2025

1. All dimensions shown in this layout plan are in meter.
2. Landuse plan of this scheme has been previously sanctioned by Housing Commissioner on dated 31/01/25.
3. This layout plan has been revised on the basis of feasibility received by Ex.En.(Electric Division- I) vide his letter no. 956/y-64/17 dated-17.06.2025 & concern given by SE. electrical circle vide his letter no.-507/R-88/20,dated-21.06.25.
4. In this layout plan 3 nos. E.S.S. (1 no. 132/33 k.v, & 2 nos.new 33/11 k.v sub-station) has been placed as per requirement given by E.E. vide his above letter & discussion with CAP.
5. Layout has been revised for provision of following 03 no. electric sub stations.
   (a) Sector-3D - 132/33 KV (5.08 Acre).This will replace 182 numbers of residential plot in sector-3D .
   (b) Sector-3B - 33/11 (2400.0 Sqm.) (P-7) provided in green open space.
   (c) Sector-2C - 33/11 (2400.0 Sqm.) (P-16) provided in green open space.
6. Detail numbering of the whole layout plan has been prepared as per request received by E.E.C.D.-8 vide his letter no. 834/y-lp(1)/285 dated- 21.04.2025 & vide his letter no.-928/y-l.p.(1) 295 , dated-02.05.2025.
7. This revised layout with 3 nos. E.S.S. & numbering plan has been finalized on the basis of feasibility received from Ex.En. vide his letter no.-1214/y-lp(i)/69 dated -28/06/2025 & concern given by SE. awadh vihar vide his letter no. -2039/y-48/21 dated - 28/06/2025 .
8. If any discrepancy is found in drawing or mismatch from site it should be informed to architect planner , upavp architecture and planning unit-4,neelgiri complex,Indira Nagar, lucknow. mail:ap4@upavp.com, immediataly.
9. This drawing will supersede drawing no.-UPHDB/APD/UN-4/LPS/NJRY/LOP/04/2025 sanctioned on 31.01.2025
10. नियोजित सेक्टरों के विन्यास की आन्तरिक फिजिबिल्टी का सत्यापन, सन्दर्भित योजना के भू–स्वामियों से अनुबन्धों / सहमति की कार्यवाही पूर्ण होने उपरान्त अन्तिम रुप प्रदान किया जा सकेगा।
11. भवन निर्माण एवं विकास उपविधि के प्रस्तर–2.1.5(I) के अनुसार मानचित्र में निर्माण विकास हेतु एक बार दी गई अनुज्ञा पाँच वर्ष के लिए वैध होती है अतः उक्त मानचित्र में निर्माण / विकास हेतु वैधता अवधि दिनांक .....से दि० ..... तक है।

PROPERTY DETAIL OF SECTOR (1 TO 5)

RESIDENTIAL PLOT

PLOT SIZE	SEC-1A	SEC-1B	SEC-1C	SEC-2A	SEC-2B	SEC-2C	SEC-3A	SEC-3B	SEC-3C	SEC-3D	SEC-4A	SEC-4B	SEC-5A	SEC-5B	SEC-5C	TOTAL
12.50 X 24.00				COMMERCIAL PLOTS	6	5	COMMERCIAL PLOTS	69	55			5				140
10.00 X 20.00					45	53		350	57	7		58				570
7.19 X 17.00	23	41	63						315						15	457
6.00 X 12.50	248	69	257							40						614
5.41 X 11.20										15					214	229
4.85 X 8.40															80	80
TOTAL	271	110	320		51	58		419	427	62		63			309	2090

PARTICULARS		AREA (HECT.)
AREA AS PER DRAWING	(A)	134.203
AREA FOR OFFICE USE UNDER MASTER PLAN 2031		23.0828
FOREST LAND (KHASRA No.-527, 528,530 & 535)		19.804
EXISTING GAUSHALA(KHASRA No.- 2)		2.3648
AREA TO BE PLANED IN FUTURE (GAUSHALA)(KHASRA No.-83)		1.5664
AREA LEFT DUE TO FOREST LAND (KHASRA No.- 536)		0.114
	TOTAL(B)	46.932
PLANNING AREA OF SCHEME(C=A-B)		87.271

Drawing Title

LAYOUT FOR SAUMITRA VIHAR YOJNA(NEW JAIL ROAD BHOOMI VIKAS EVAM GRIHSTHAN YOJNA) MOHANLAL GANJ LUCKNOW (AREA 87.271 HECTARE)

Drawing For: APPROVAL ● CONSTRUCTION ○ TENDER ○

Scale: N.T.S

Date: 21-07-2026

Drawing No.: UPHDB/APD/UN-4/LPS/NJRY/LOP/ /

Revision: 4

LAST REVISION 15-07-2025

North

IS 15700:2018

UPAVP
ARCHITECTURAL AND PLANNING SECTION NEELGIRI COMPLEX, INDIRA NAGAR LUCKNOW-226016

PREPARED BY
ARCHITECT
AR. ASHUTOSH VERMA

DnC Group
DESIGN 'N' CREATION GROUP
C-1/142, VIKRANT KHAND, GOMTI NAGAR, LUCKNOW
+919415106890, +0522-230-6789

Vikas singh, D.MAN	SD.- 21-07-2026	
Mamta Verma, Dip. Arch., Arch. Architect Planner	SD.- 21-07-2026	
Jyoti Katiyar, B. Arch., Architect Planner	SD.- 21-07-2026	
Sanjeev Kashyap, B. Planning, M. Planning (Environmental Planning) A.I.T.P., Sr. Architect Planner	SD.- 21-07-2026	
Sanjeev Kashyap, B. Planning, M. Planning (Environmental Planning) A.I.T.P., Chief Architect Planner		
Dr. Balkar Singh, I. A. S., Avas Ayukt	SD.- 21-07-2026	

IS15700:2018
सेवोत्तम प्रमाणित

उत्तर प्रदेश आवास एवं विकास परिषद

कार्यालय अधिशासी अभियन्ता, निर्माण खण्ड लखनऊ–8
एंकर शाप नं0–1, 2, 3 एवं 4 अवध शिल्प ग्राम, अवध विहार योजना, लखनऊ।
Email-officecdlko8uphdb@gmail.com

भारतीय मानक ब्यरो IS 15700
SQMS

पत्रांक : 2325 / Y-23 / 71 दिनांक : 08-10-2026

Area Justification For Saumitra Vihar Yojna, Mohanlalganj, Lucknow in RERA

Area Justification (Hec.)

1	Total Area of planned portion as sanctioned Layout plan		85.9966
2	Add area for RERA registration (Master Plan Area)		
	STP	(+)	0.4314
	OHT	(+)	0.2354
	Road	(+)	1.0164
	Green	(+)	0.8000
	Total (A)		**88.4798**
3	**Deduct Area which is not in possession of Parishad and not in RERA registration**		
	(Road and Park in Sithauli Khurd) Details enclosed	(-)	6.5312
	School in sector- 3A	(-)	1.3745
	Road	(-)	0.0612
	Plots (54.00+63.00)/2x129	(-)	0.7546
	Plots (27.00+18.00)/2x106	(-)	0.2363
	School in sector- 3A	(-)	0.2887
	Plots (130.00x20.00)	(-)	0.2600
	Park in sector- 3A	(-)	0.2530
	Park P-05	(-)	0.1930
	Plot 3B/84 tp 86	(-)	0.0600
	Total deduction (B)	**(-)**	**10.0125**
4	**Net Area for RERA registration (A-B)**		**78.4673**

Executive Engineer
Construction Division Lko-8
U.P. Avas Vikas Evam Parishad
Awadh Shilp Gram
Awadh Vihar Yojna Lucknow